

01 面积闭合

上翼与连接段合并使用，面积不再拆开造成误差

主吧+特调（含边带）	19. 90
前场咖啡与交流 · 18席	78. 39
半开放拼装 · 10席	25. 23
员工打磨修复	29. 92
珍藏与格纳库	81. 00
修复停看带	2. 36
故事回廊与公共通行	30. 80
故事阅读与观展咖啡 · 12席	84. 90
修复门专属末段	0. 90
合计（上翼H按6000暂算）	353. 40

分区参考面积，含区内通行；未扣墙柱及井道。
上翼53. 40+下接31. 50=右上公共区84. 90。

02 用故事串起参观

S1 修复前后

从公共旁路进入站看带，隔玻璃向左看。

S2 拼装背面的故事墙

墙外讲零件、制作和创作者，回廊从外侧绕行。


S3 为什么收藏

收藏者照片与短 timeline，坐下翻图册。

S4 设定到成品

设定图、成品对照、短片及尺度细节。

仅规划展示载体和位置；图文与真实收藏资料另行整理。

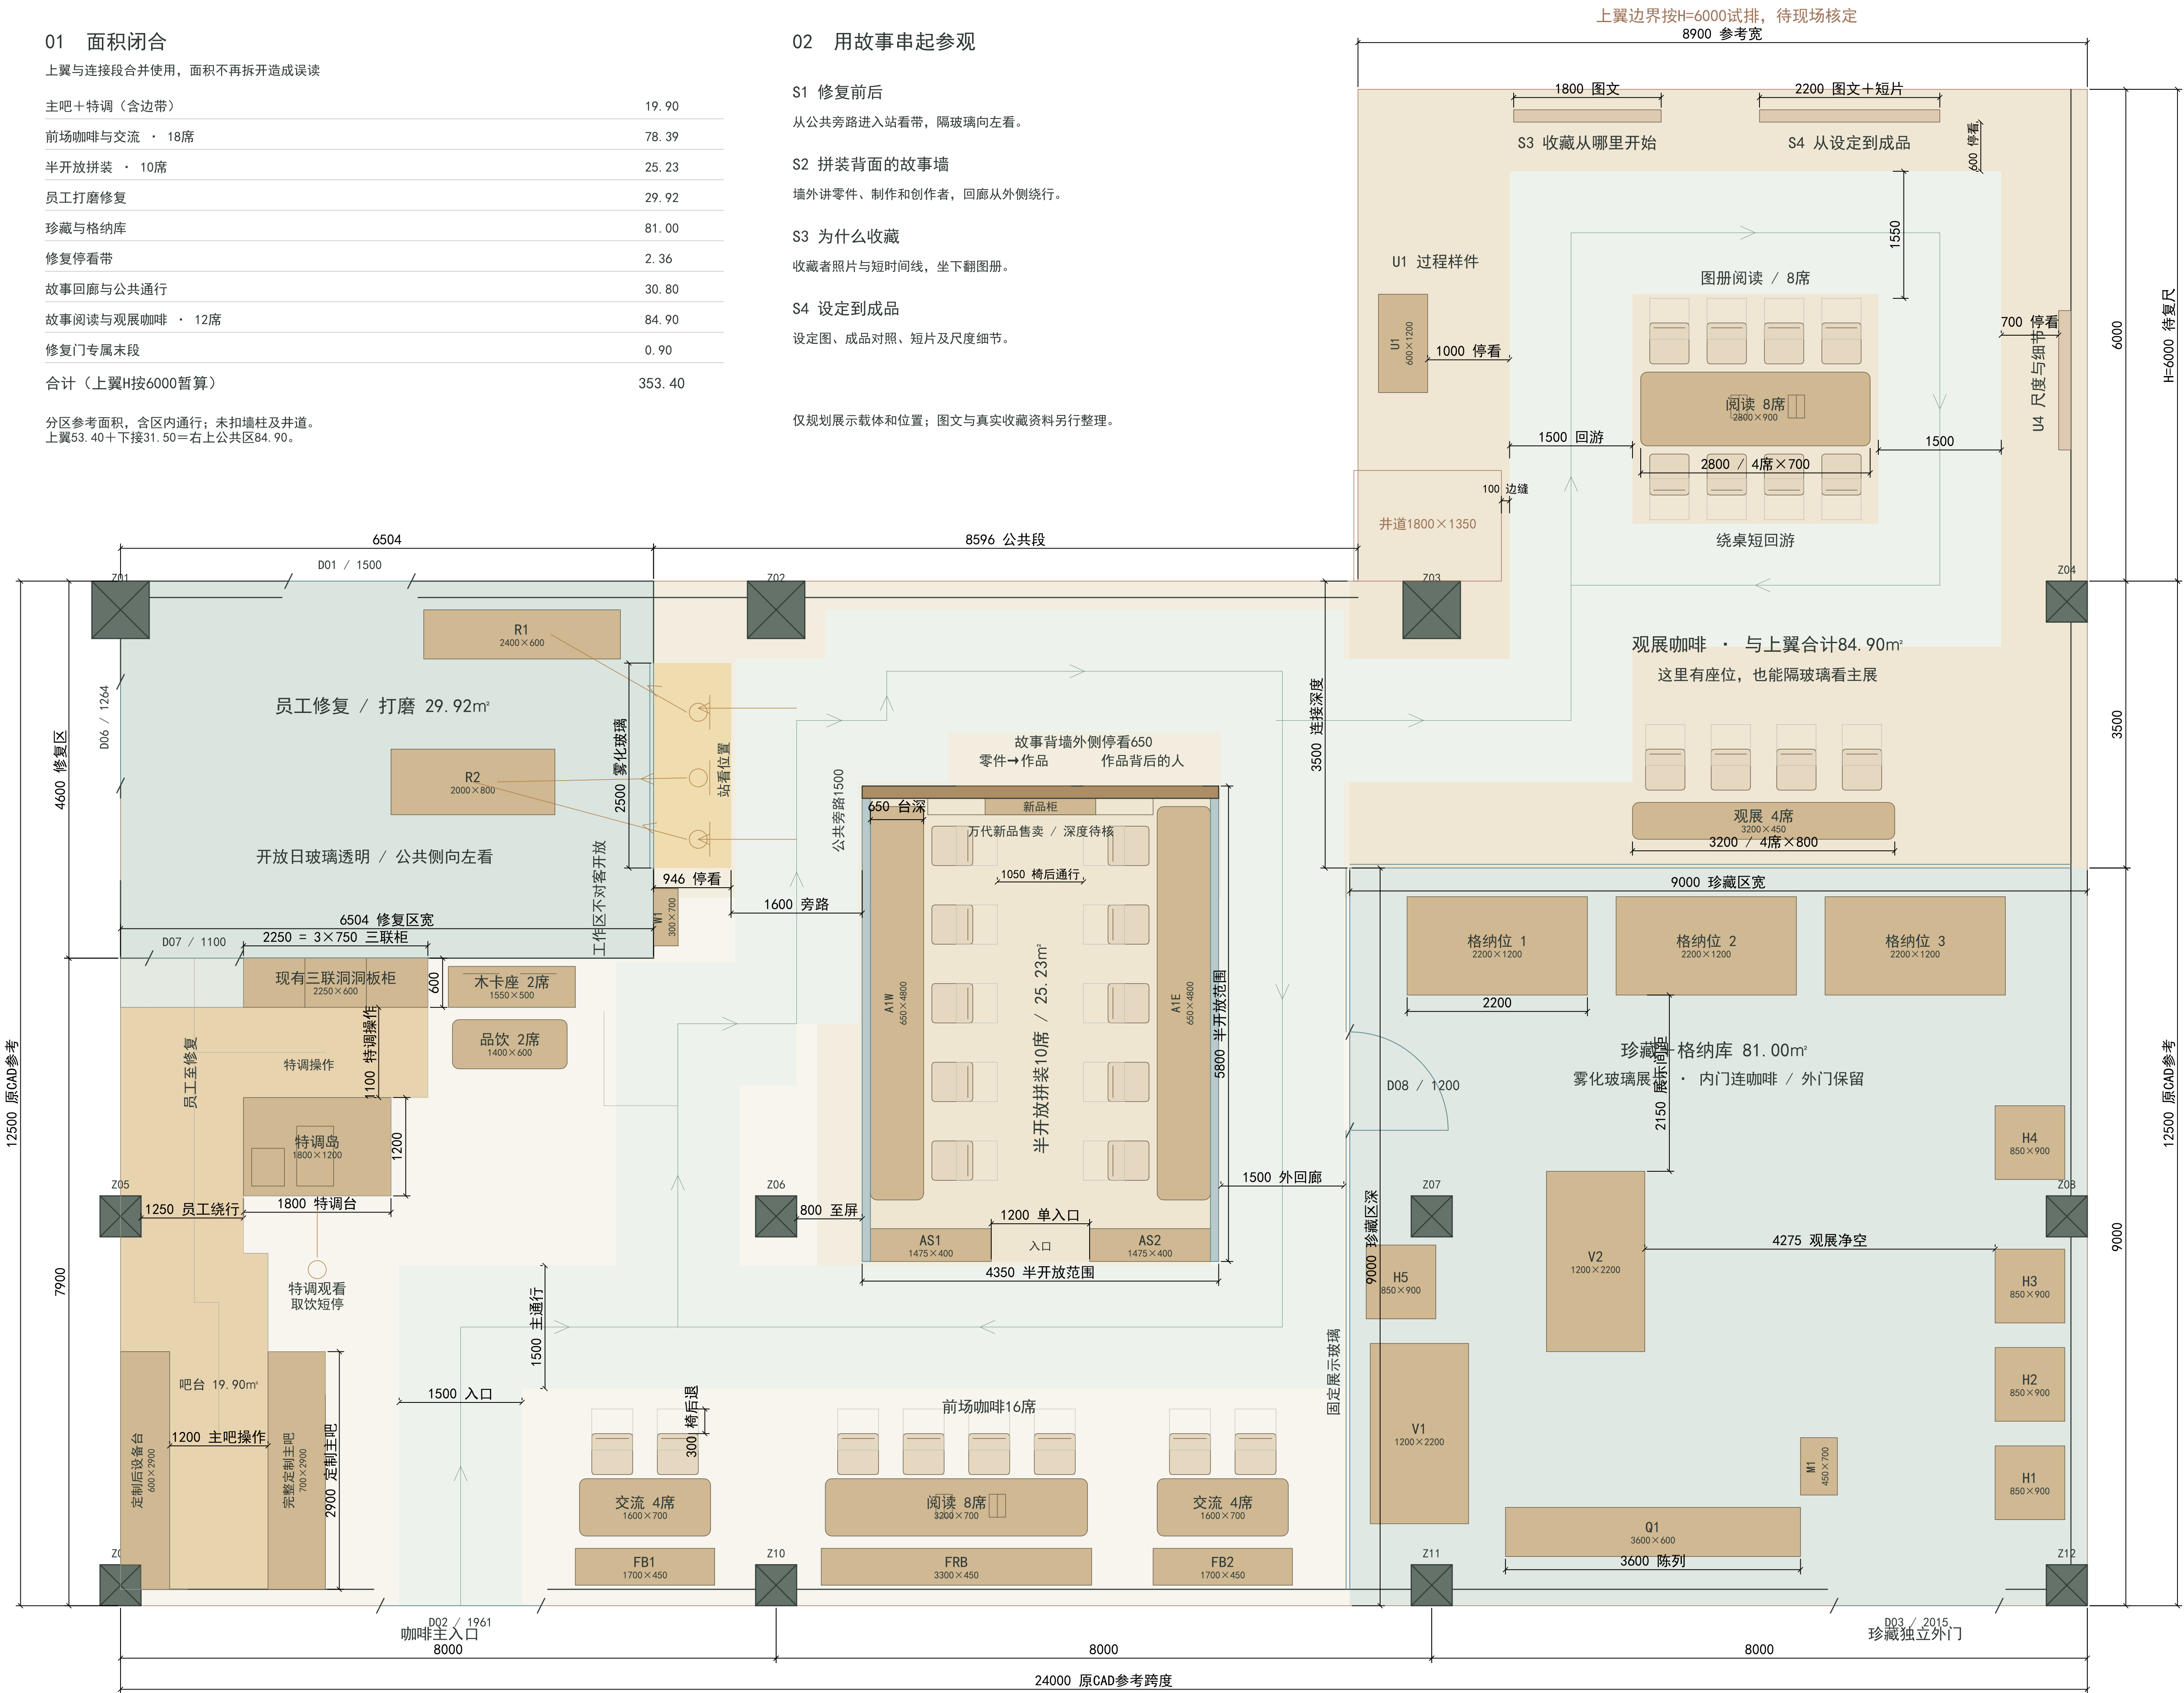

本版空间安排

30 咖啡席

前场16+特调旁2+右上12

10 半开放拼装位

不计入咖啡座位数

吧台与特调

主吧完整定制，复用柜归特调。
三联柜2250×600，总高2600；
3段各750，资料来自用户PDF首图。
柜贴修复南侧，特调在它前方；
两者之间留1100操作距离。
特调1800×1200，水槽/冰槽示意。
咖啡范围（含边带）19. 90m²。

半开放拼装 / 回廊

左右各5席，台面4800×650。
南侧单入口1200，集中借还工具。
前/侧低柜与透明屏，上部敞开；
北墙内侧万代新品货架（设计示意）；
外侧650故事停看带，
再外侧1500回廊，不穿过工位。
椅各后退300后，中间仍净1050。
货盒深度待核；10席仍仅简单拼接。

公共展示的载体

U1 600×1200样件保护台
U2 1800短图文板
U3 2200图文+短片
U4 1700尺度细节板
浅板仅150深，保留独立停看带。
阅读桌放可拿取图册；观展席直接看玻璃后的格纳库。

保留关系

修复窗外的金色人位即观看位置。
游客从旁路侧向进入、面向左看；
开放日玻璃透明，工作区不进入。
珍藏81m²保留D03独立外门。
D08新增西侧内门1200通咖啡，
南较向馆内开，外回廊1500不变。
咖啡仍30席，其余原R17布局不变。
木椅与木卡座，不用皮椅。

图例 / 数据边界

- 墙 / 原柱
- 展示 / 雾化玻璃
- 公共回游方向
- 椅后退包络
- 边界或尺寸待核

尺寸按CAD与已知家具试排。
上翼深度、井道与柜体实物待复尺；本页不包含施工做法。