

01 面积闭合

上翼与连接段合并使用，面积不再拆开造成误差

主吧+特调（含边带）	19.90
前场咖啡与交流 · 18席	78.39
半开放拼装 · 10席	25.23
员工打磨修复	29.92
珍藏与格纳库	81.00
修复停看带	2.36
故事回廊与公共通行	30.80
故事阅读与观展咖啡 · 12席	84.90
修复门专属末段	0.90
合计（上翼H按6000暂算）	353.40

分区参考面积，含区内通行；未扣墙柱及井道。
上翼53.40+下接31.50=右上公共区84.90。

02 用故事串起参观

S1 修复前后

从公共旁路进入站看带，隔玻璃向左看。

S2 拼装背面的故事墙

墙外讲零件、制作和创作者，回廊从外侧绕行。


S3 为什么收藏

收藏者照片与短 timeline，坐下翻图册。

S4 设定到成品

设定图、成品对照、短片及尺度细节。

仅规划展示载体和位置；图文与真实收藏资料另行整理。

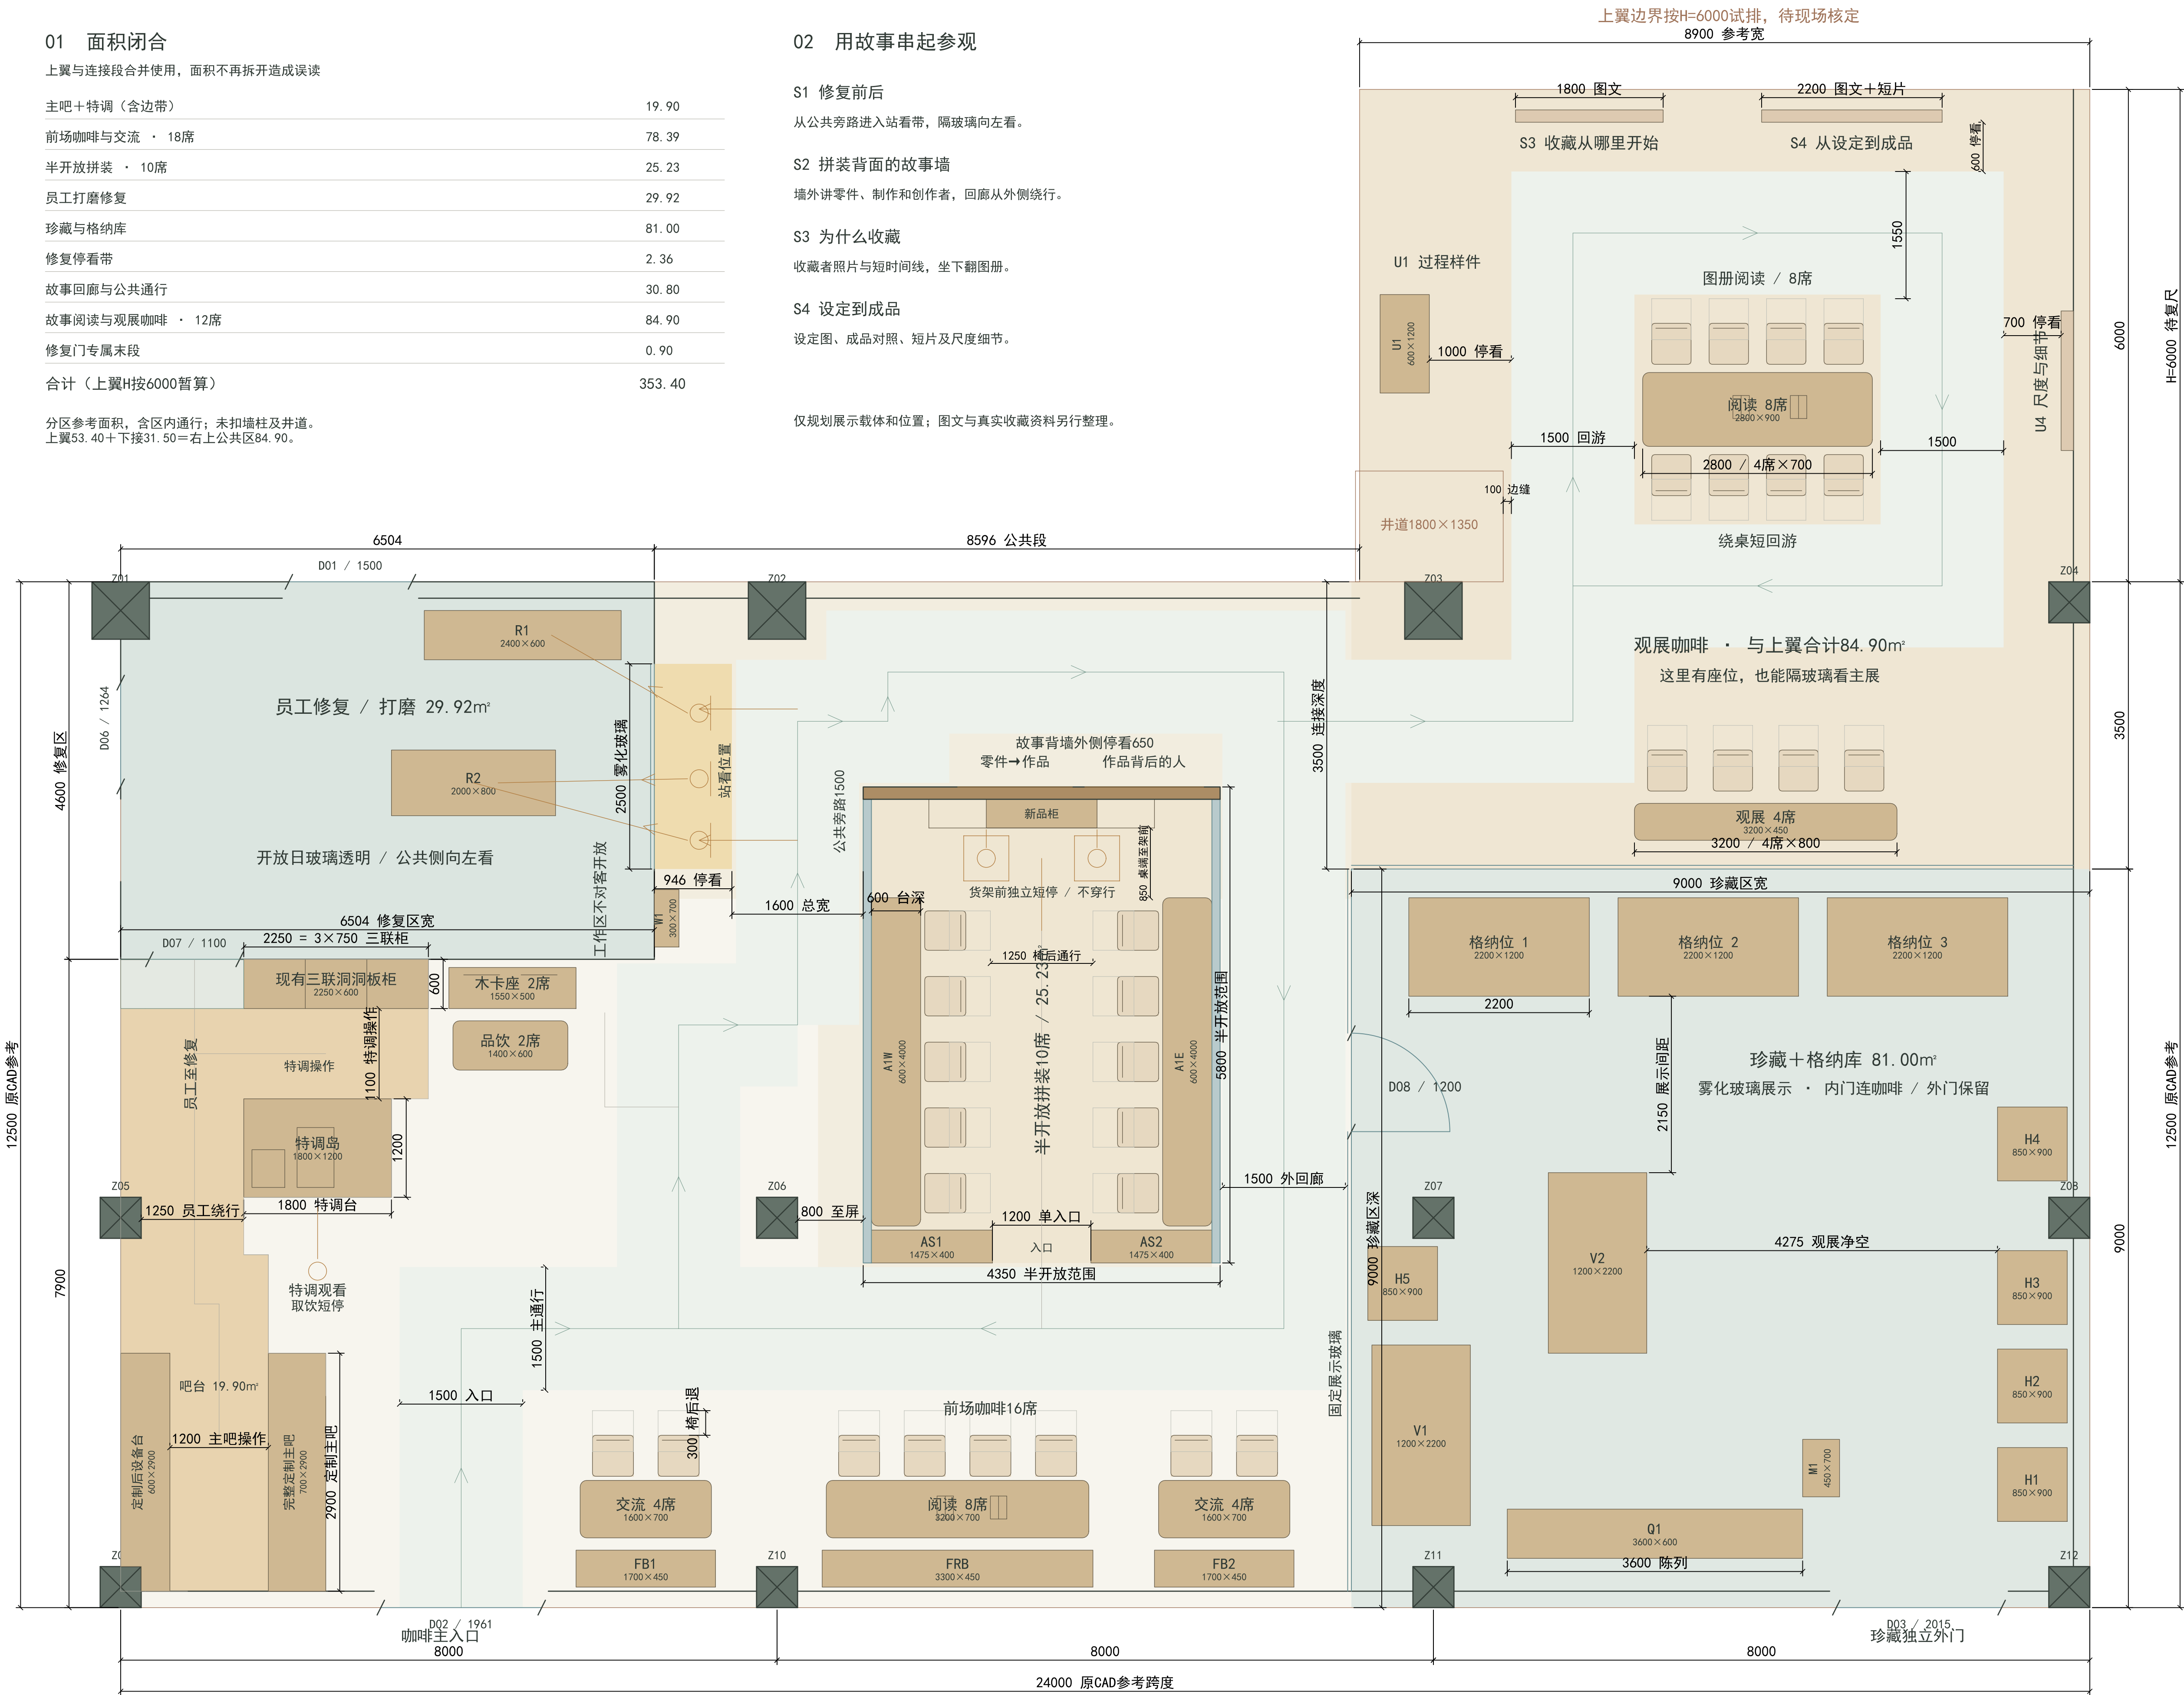

本版空间安排

30 咖啡席

前场16+特调旁2+右上12

10 半开放拼装位

不计入咖啡座位数

吧台与特调

主吧完整定制，复用柜归特调。
三联柜2250×600，总高2600；
3段各750，资料来自用户PDF首图。
柜贴修复南侧，特调在它前方；
两者之间留1100操作距离。
特调1800×1200，水槽/冰槽示意。
两主操作位+第三人分时补给。
1100内需让行，不称背后自由错身。
咖啡范围（含边带）19.90㎡。

半开放拼装 / 回廊

左右各5席，台面4000×600。
每席节距800；南侧单入口1200。
前/侧低柜透明屏，上部敞开；
北墙内侧售卖架350深，盒型待核。
未排椅至架前1010；桌端至架前850。
另设两处短停，与未排到座分开。
椅各后退300后，中间净1250。
墙外AN1/AN2讲故事，外回廊1500。
只做简单拼接，不喷涂打磨。

公共展示的载体

U1 600×1200样件保护台
U2 1800短图文板
U3 2200图文+短片
U4 1700尺度细节板
浅板仅150深，保留独立停看带。
阅读桌放可拿取图册；观展席直接看玻璃后的格纳库。

保留关系

修复窗外的金色人位即观看位置。
游客从旁路侧向进入、面向左看；
开放日玻璃透明，工作区不进入。
珍藏81㎡保留D03独立外门。
D08新增西侧内门1200通咖啡，
南较向馆内开，外回廊1500不变。
咖啡仍30席；建筑壳与柱位不变。
木椅与木卡座，不用皮椅。

图例 / 数据边界

- 墙 / 原柱
- 展示 / 雾化玻璃
- 公共回游方向
- 椅后退包络
- 边界或尺寸待核

尺寸为设计值，并非全量现场复尺。
1051门对应D02；两内柱暂对应。
墙垛、凹入、梁底及盒型仍待核。